


GEOTHERM 2027 · STAND 274 · ORDER SUMMARY AND SKETCH

Exhibitor: Enedril · Regi No 48661 · 18 m² (3 × 6 m), end of block · DRAFT to check against the order forms

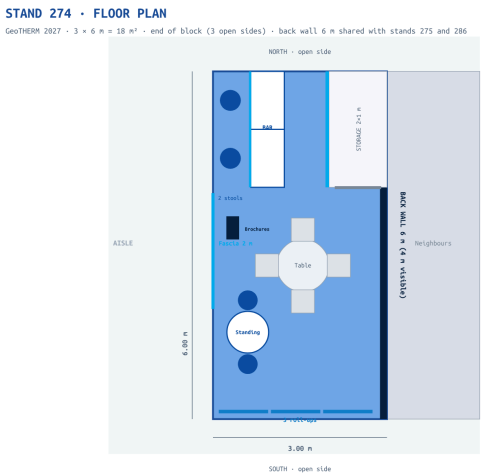

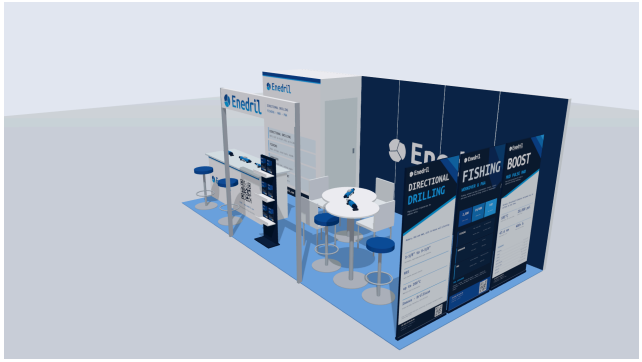

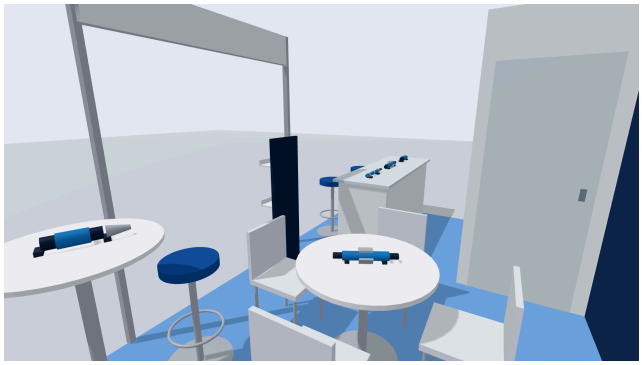


Left: floor plan, north up (open sides west, north, south; back wall 6 m shared with stands 275 and 286). **Right:** 3D illustration of the intended result. Detailed sketch with dimensions on page 2.

Pos.	Article	Qty	Unit EUR	Total EUR
106003	**System stand type 3, 18 m²** includes: 200 × 100 cabin with door, shelf, fridge · table + 4 chairs · 2 counters (used together as reception bar) · leaflet stand · grey carpet	18 m²	153.00 / m²	2,754.00
105058	**Printed partition wall panel 100 × 250 cm** Back wall: 4 visible panels + storage face: 2 panels. Print data supplied by Enedril	6	330.00	1,980.00
107090	**Coloured lettering / logo on fascia, max W200 × H29.9 cm** Logo file (EPS/PDF) to osing@messe-offenburg.de	1	119.00	119.00
–	**Carpet in another colour (light blue)** Shade to be specified: _____ (grey is included)	18 m²	15.00 / m²	270.00
105059	**Printed front for the 2 counters (bar)** Banner for counter, W95 × H80 in the kit: confirm 100 × 90 cm print	2	188.00	376.00
107021	**Plastic bar table, white, round, H110 Ø70** Standing table for 2 people	1	39.00	39.00
107004	**Z bar stool, black / chrome** 2 for the bar + 2 for the standing table	4	39.90	159.60
	Total (excl. VAT) Without roll-ups (printed by Enedril)			**5,697.60**

To do: tick the positions and quantities on the order forms (sections H, K, print items), attach this sketch, sign, and send to geotherm@messe-offenburg.de **before 11 December 2026** (10 % surcharge afterwards, min. 25 EUR). Print files are sent separately. Prices excl. VAT, read from the exhibitor kit; the type 3 stand already contains the 2 counters, the table with 4 chairs and the leaflet stand: please place them as shown on the sketch. Roll-ups are printed by Enedril.

SKETCH · STAND 274 (PLAN VIEW)

Scale 1:25 · dimensions in cm from the south-west corner · grid 50 cm

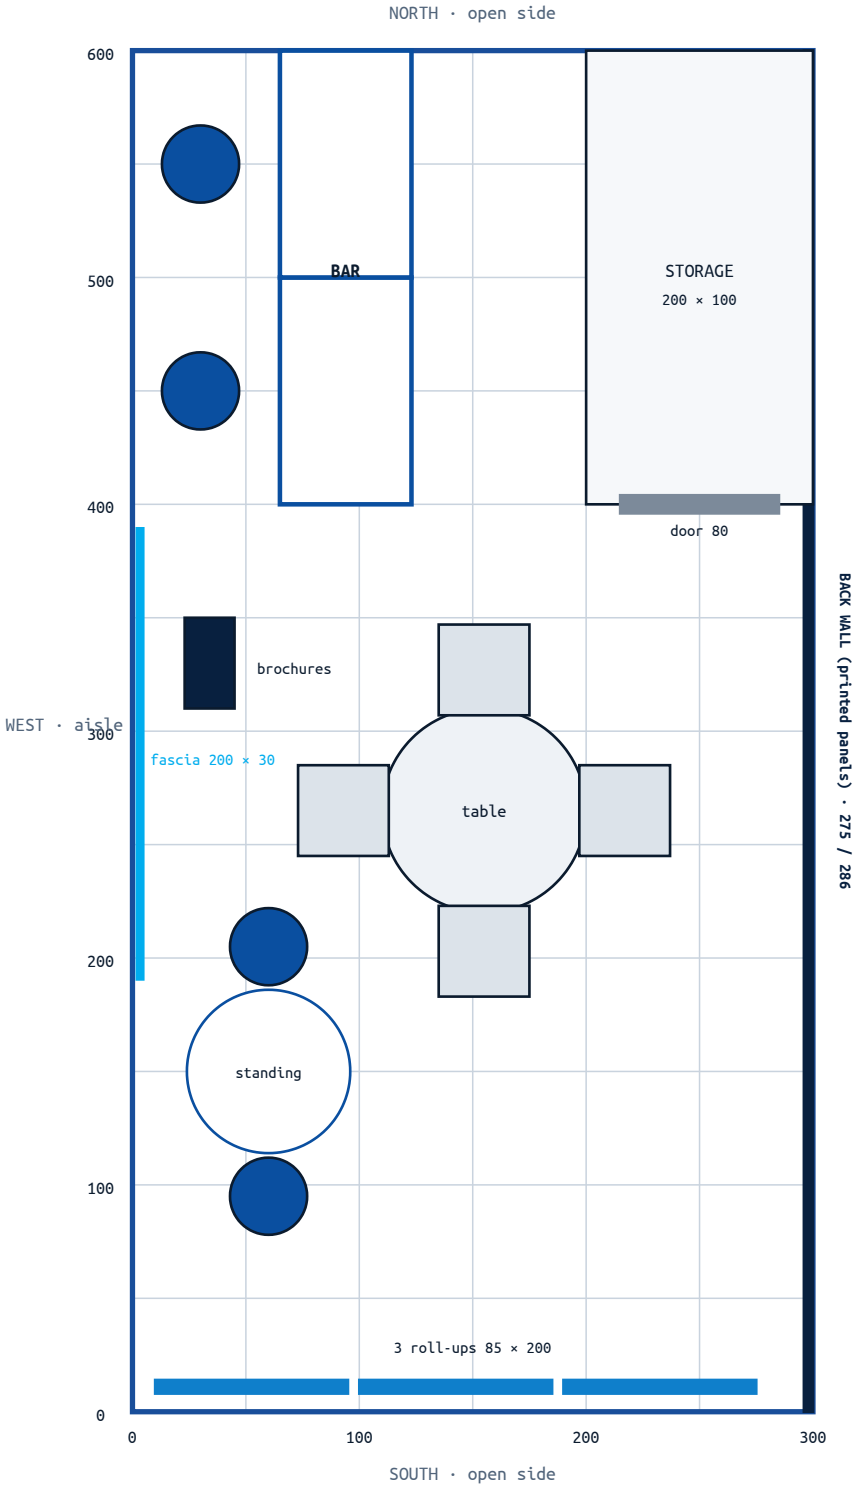


Legend and positions

Stand 18 m²	3.00 × 6.00 m, end of block; open sides west, north, south
Back wall	x = 300, full length: printed panels 100 × 250 (4 visible, 1 to 4 from south)
Storage cabin	200 × 100 cm: x 200-300, y 400-600; door 80 cm on the south face; west face printed (2 panels)
Reception bar	2 counters 100 × 58 × 90 end to end: x 65-123, y 400-600; west face printed 200 × 90
2 bar stools	centres (30, 450) and (30, 550)
Leaflet stand	x 23-45, y 310-350, facing west
Meeting table	round, centre (155, 265) + 4 chairs
Standing table	round H110 Ø70, centre (60, 150) + 2 bar stools at (60, 95) and (60, 205)
3 roll-ups	85 × 200, along the south edge: x 10-95, 100-185, 190-275 (y 8-14), facing south
Fascia	200 × 29.9 cm above the west opening, y 190-390, height 220-250 cm

SKETCH TO REDRAW · STAND 274

Blank grid, same scale: draw partitions, furniture, doors and lettering as on page 2

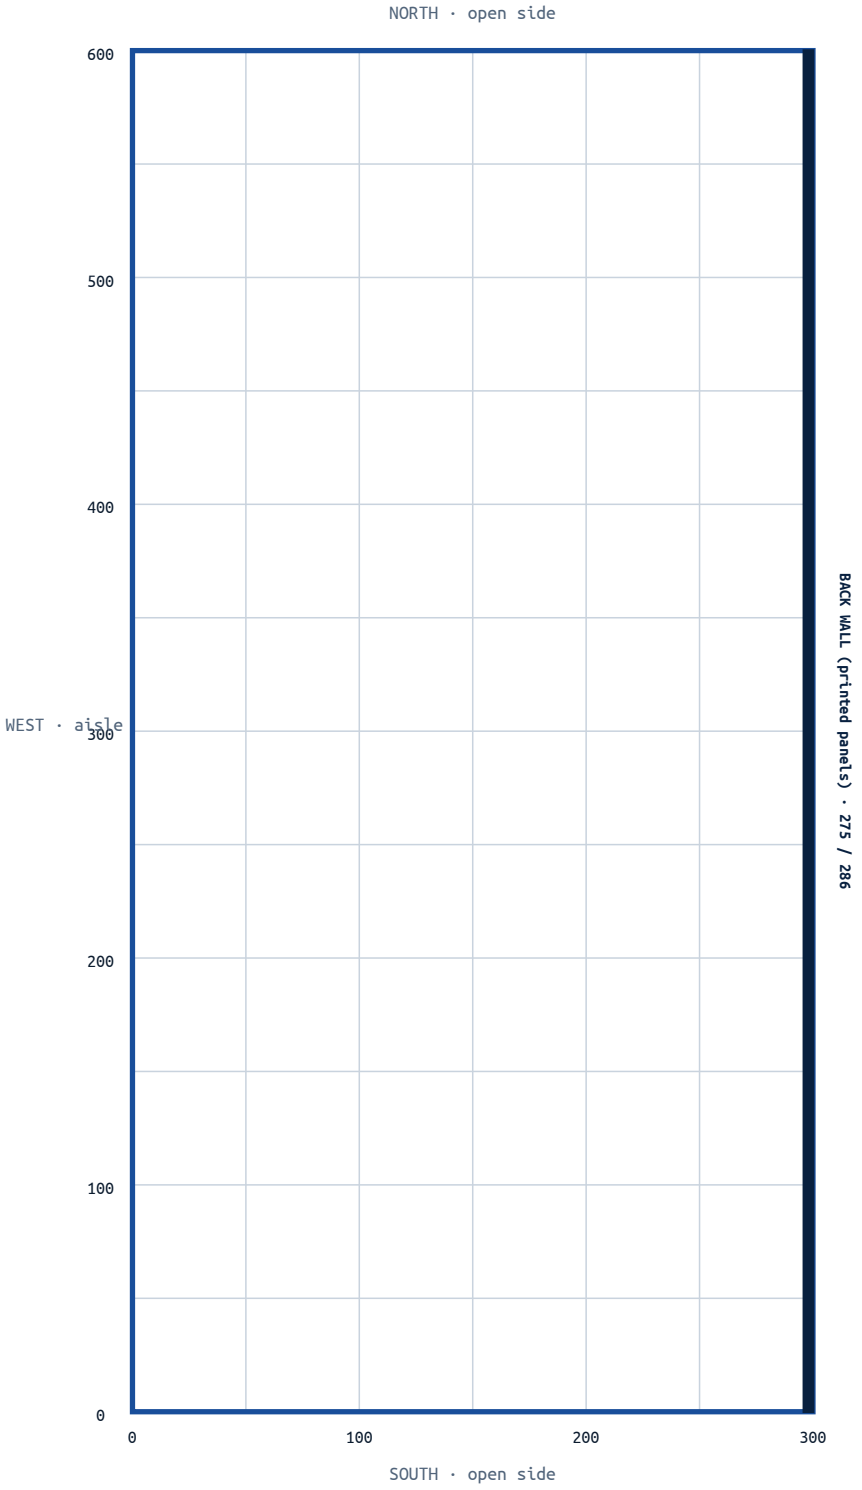

Symbols asked by the form

wall construction	thick line
aperture	gap in the line
door	arc, stop left or right
tables and chairs	circle / squares
labeling	write the text on the wall